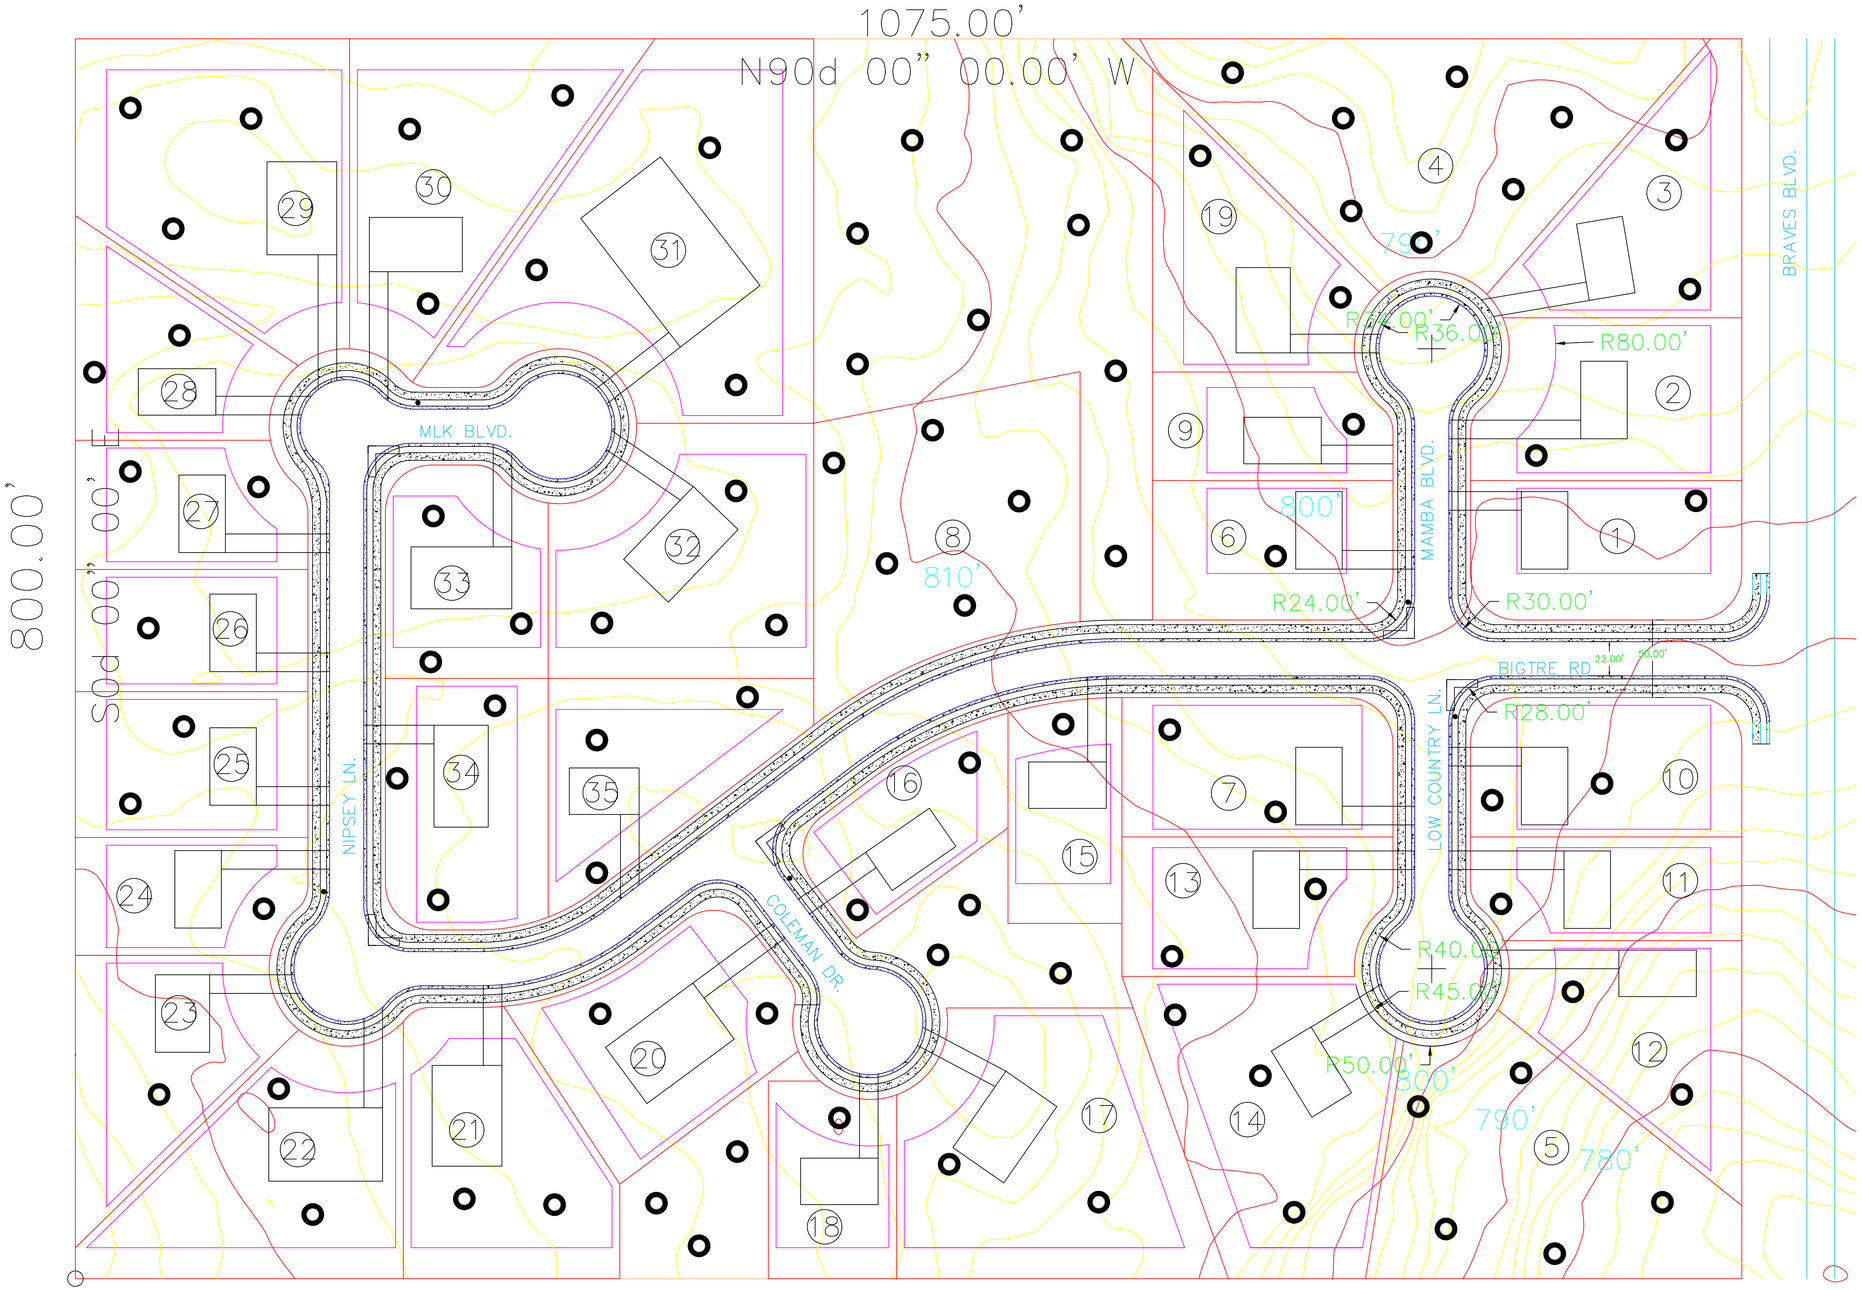


LOT AREAS	
LOT	AREA
1	14800
2	10200
3	12000
4	33000
5	27800
6	13700
7	15500
8	28900
9	10300
10	14000
11	11300
12	16000
13	14800
14	25000
15	10300
16	10300
17	30700
18	10200
19	17500
20	18400

21	20100
22	23500
23	16400
24	10900
25	14100
26	11800
27	12000
28	13200
29	30100
30	25700
31	42000
32	26000
33	13700
34	16500
35	15800

Legend
- Trees
- Sign
- Street Name Sign

General Notes
1. Total Size of the development is ____177.76095____ acres.
2. Total number of buildable lots is _____35____.
3. All lots shall take internal access. No lot shall have direct access from the subdivision to Braves Blvd.
4. Density of the development is _____5.079_____ dwelling units per acre.
5. Minimum lot size is 10,000 sq. ft.
6. Typical home footprint is 45' x 30'.
7. Site is located outside a FEMA floodzone.
8. The minimum lot width is 75' as measured at the front setback line.
9. Front yard setback is 30'.
10. Side yard setback is 5'.
11. Back yard setback is 20'.
12. Subdivision is zone R-4.
13. Subdivision is located within an area with county zoning and ordinance laws.